فيوتشر باور
FUTURE POWER

OFFER NUMBER: IEC_bas001

PROJECT NAME: **gradution project**

CLIENT NAME: Geranito

CONSULTANT:

CONTRACTOR:

Action Code / Approval By Customer :

[A] Approved
[B] Approved As Noted
[C] Revise & Resubmit
[D] Disapproved
[E] Info Required
[F] Noted

DATE: ----------

SIGNATURE: ----------

SPACE FOR COMMENTS :

ENGINEERING OFFICE

Designed By: Abdelrahman Hosny

Approved By: DR.Tarek Ahmed

DATE: 10/28/2026

Scan to visit our website

TECHNICAL DATA

Enclosure Type :

Rated Operational Voltage : **380V**

Rated Control Voltage : **24V**

Rated Frequancy : **50 Hz**

Painting RAL Number : **Ral7035**

Enclosure Material: **Sheet Steel _ 1.5 mm**

Installation Type:

Mounting:

Degree of Protection:

Panel Dimension:

Height (mm): **Geranito**

Width (mm):


Depth (mm):

Form of Seperation:


Ambient Temprature: **40 °C**

2


			Date	10/22/2026	EPLAN	geranito	Title page	= CA1
			Ed.	IGFI				+ EAA
			Appr.		graduation project			IEC_bas001 Page 1
Modification	Date	Name	Original		Replacement of	Replaced by		Page 1 / 11

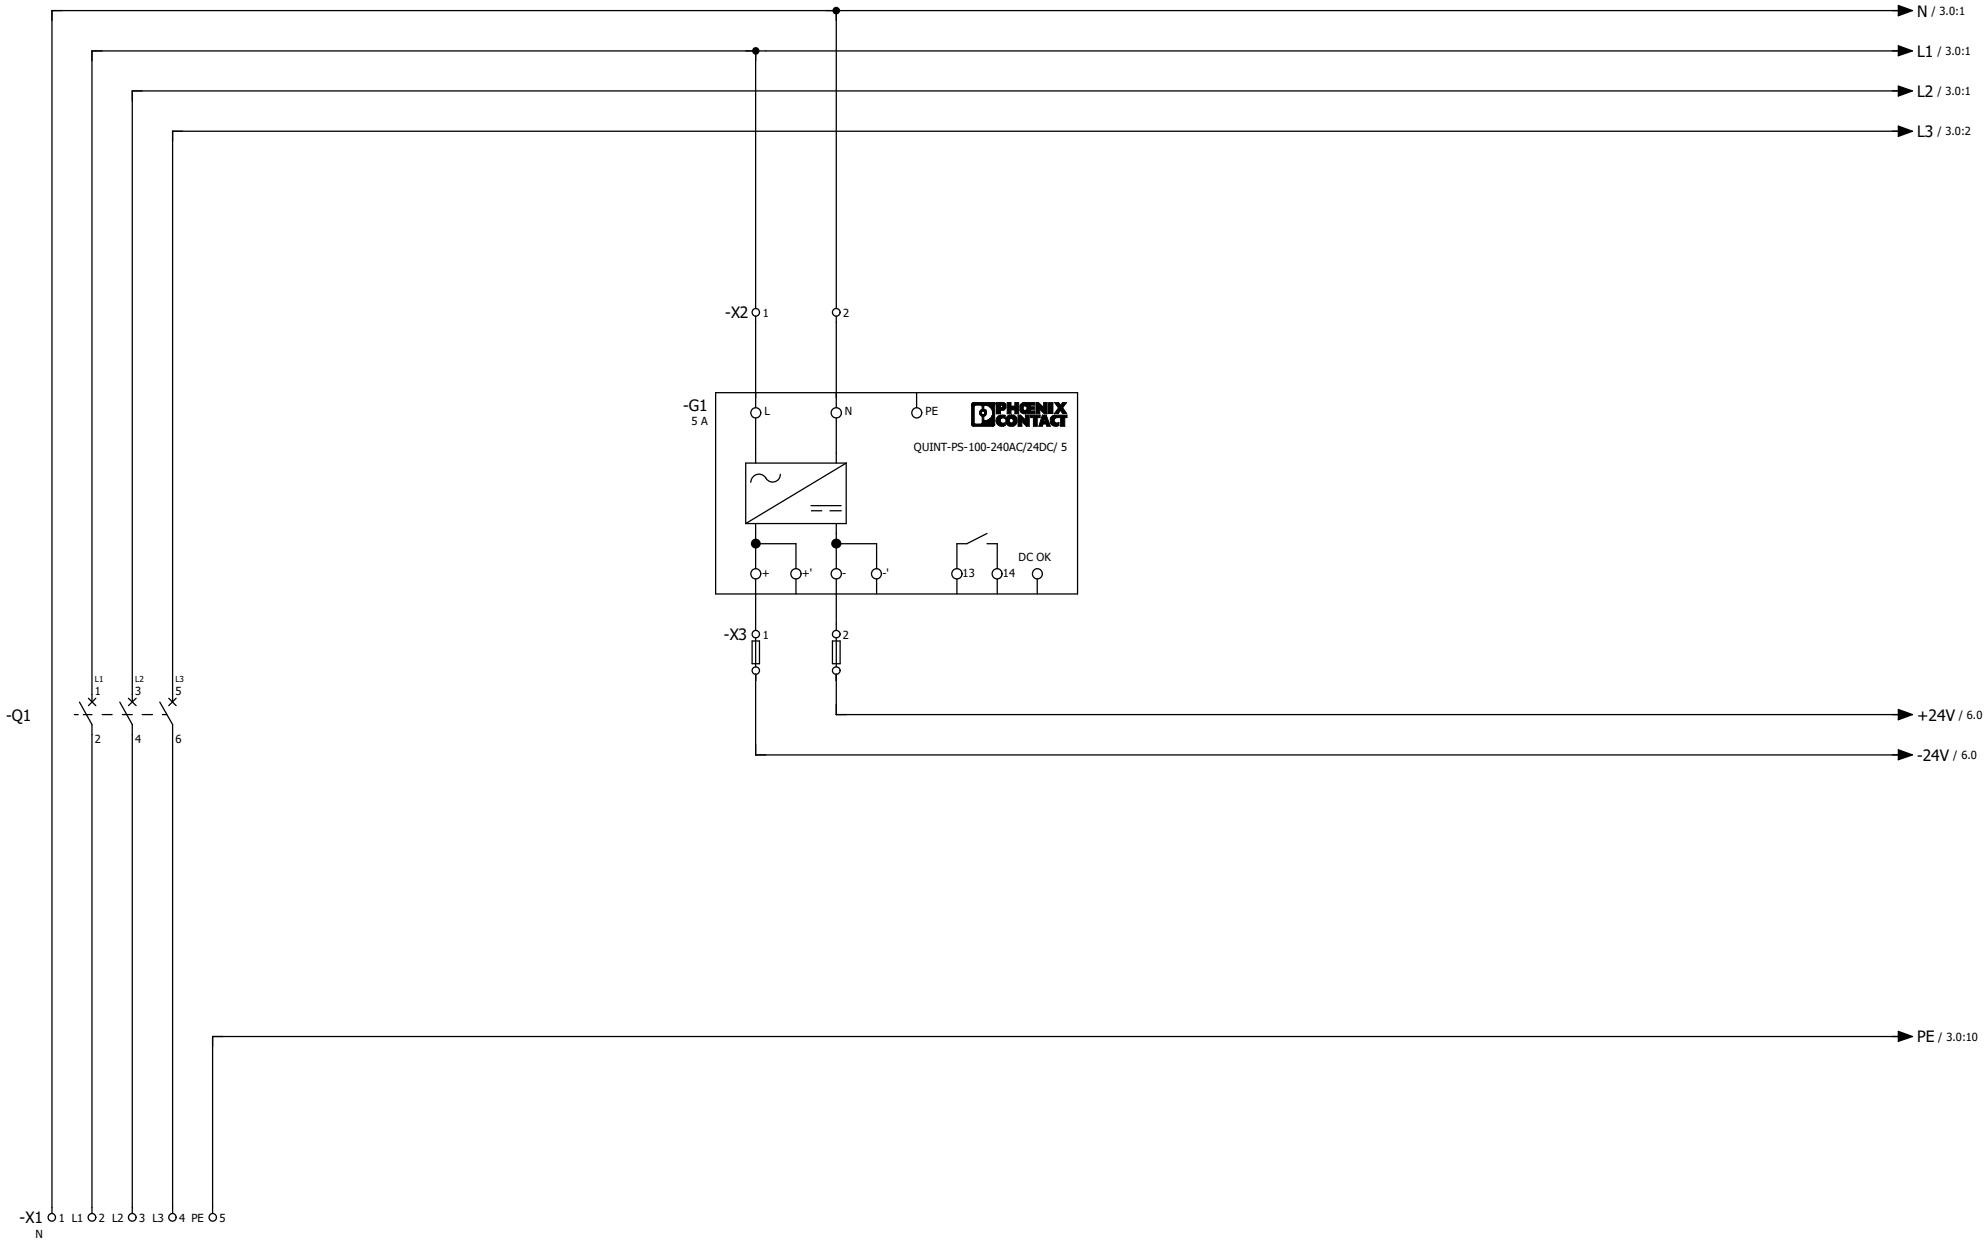

Date:	10/28/2026		Page description: main power		Project NAME : gradution project	Page Number 2	Page Name 2
Designed by:	Eng: A.Hosny				Client: Geranito		Current Sheet 2
Approv.	DR: T.Ahmed						Total Sheets 11

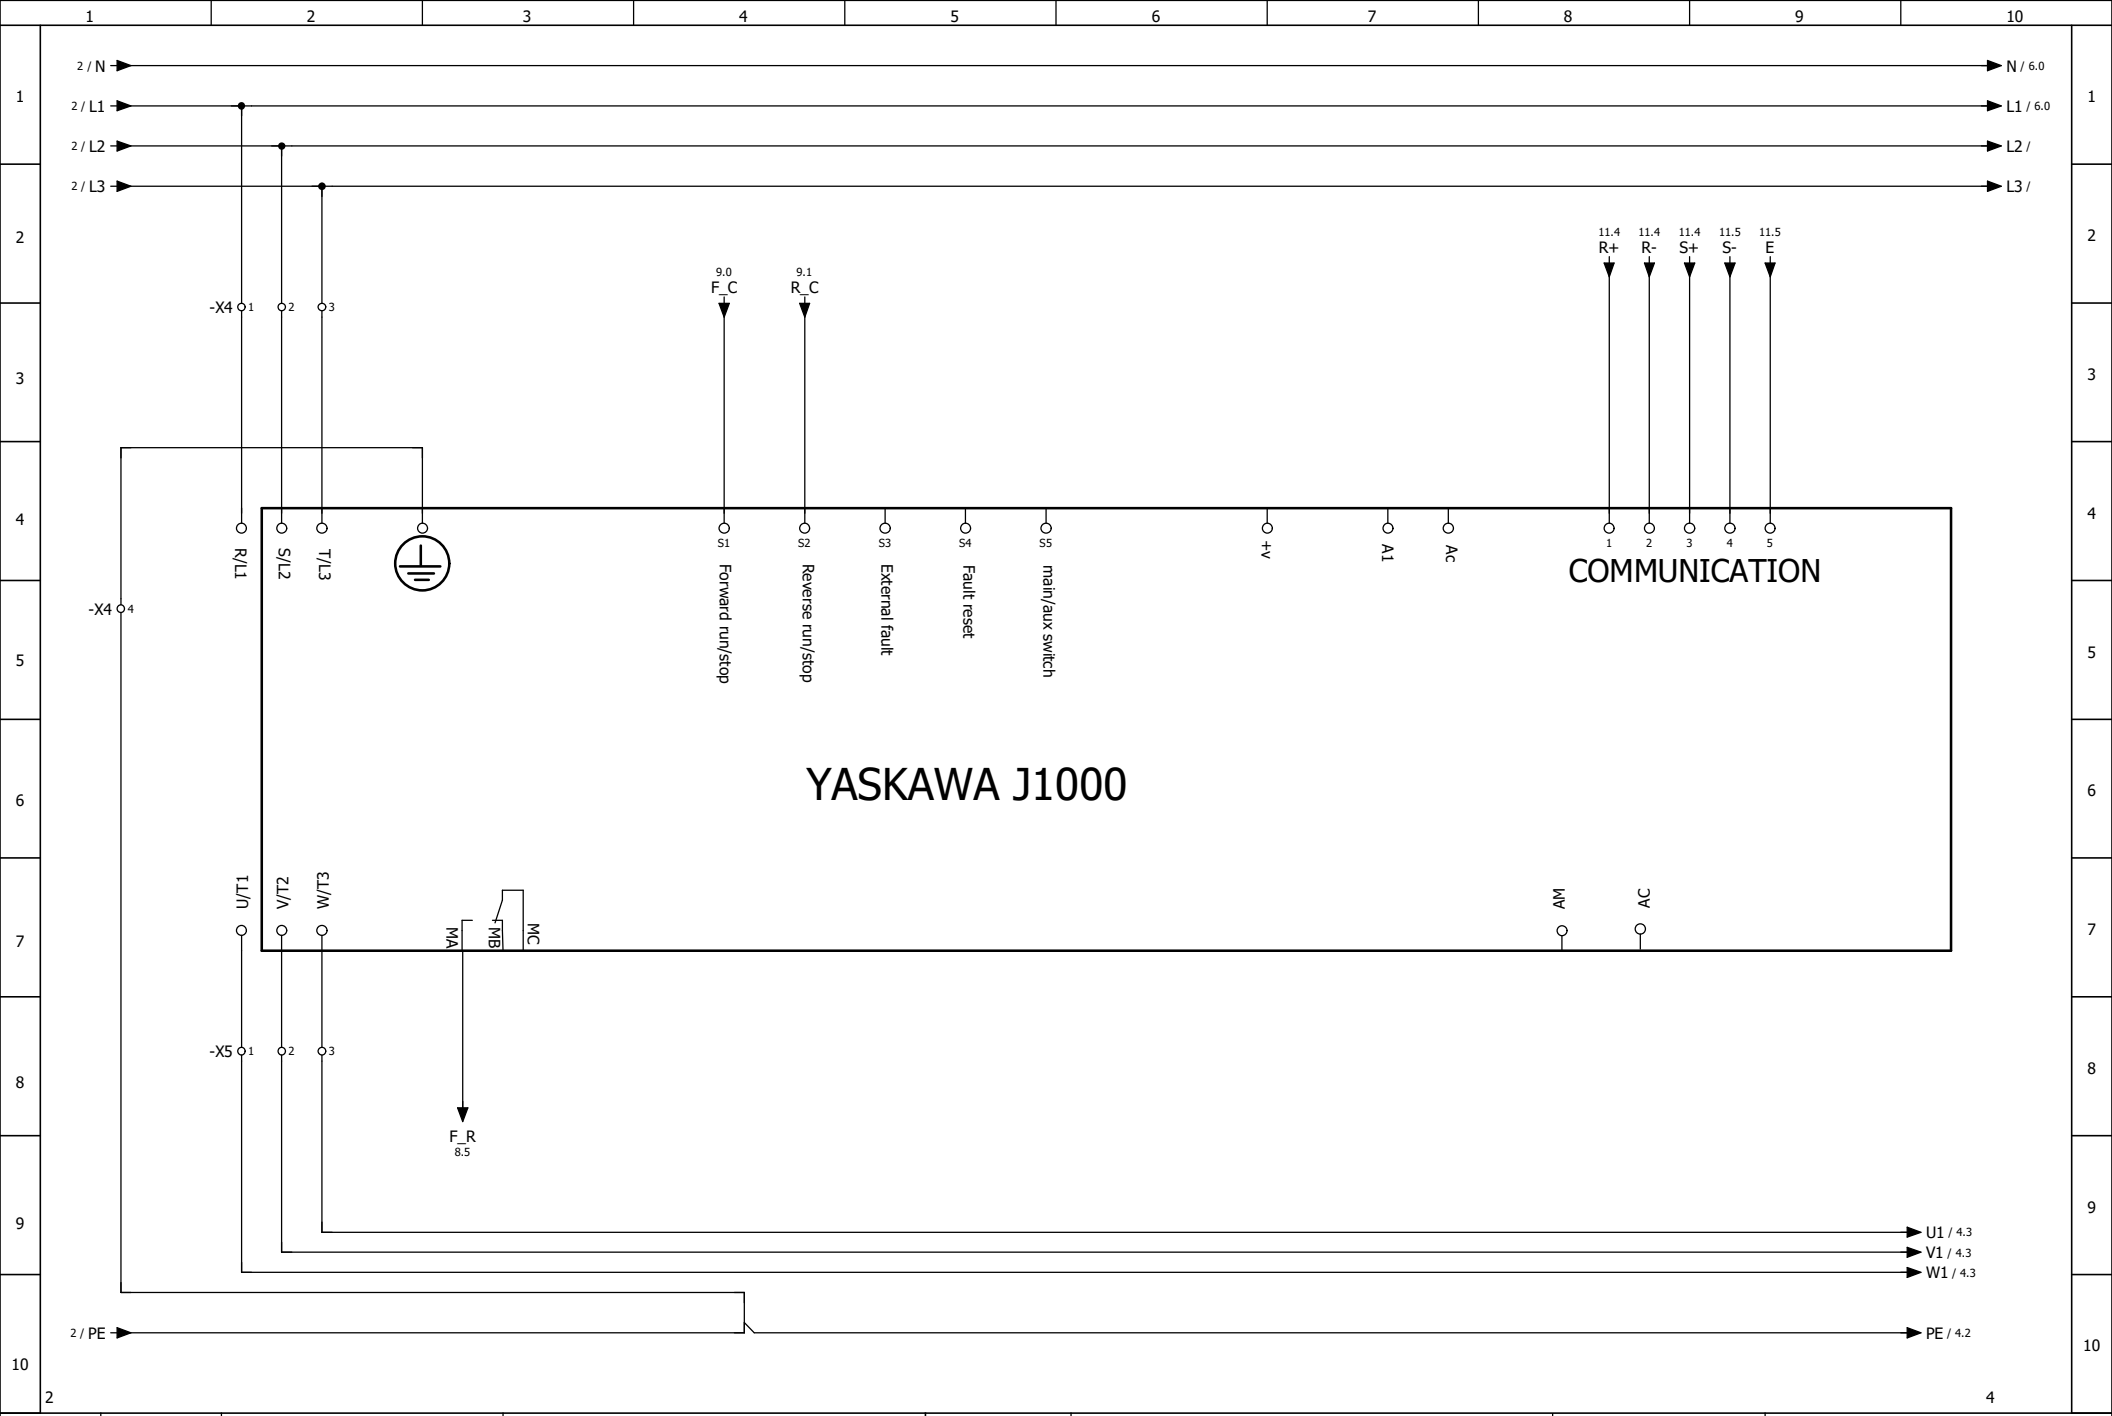


Date:	10/28/2026	Page description: power_drive		Project NAME : gradution project	Page Number 3	Page Name 3
Designed by:	Eng: A.Hosny			Client: Geranito		Current Sheet 3
Approv.	DR: T.Ahmed					Total Sheets 11

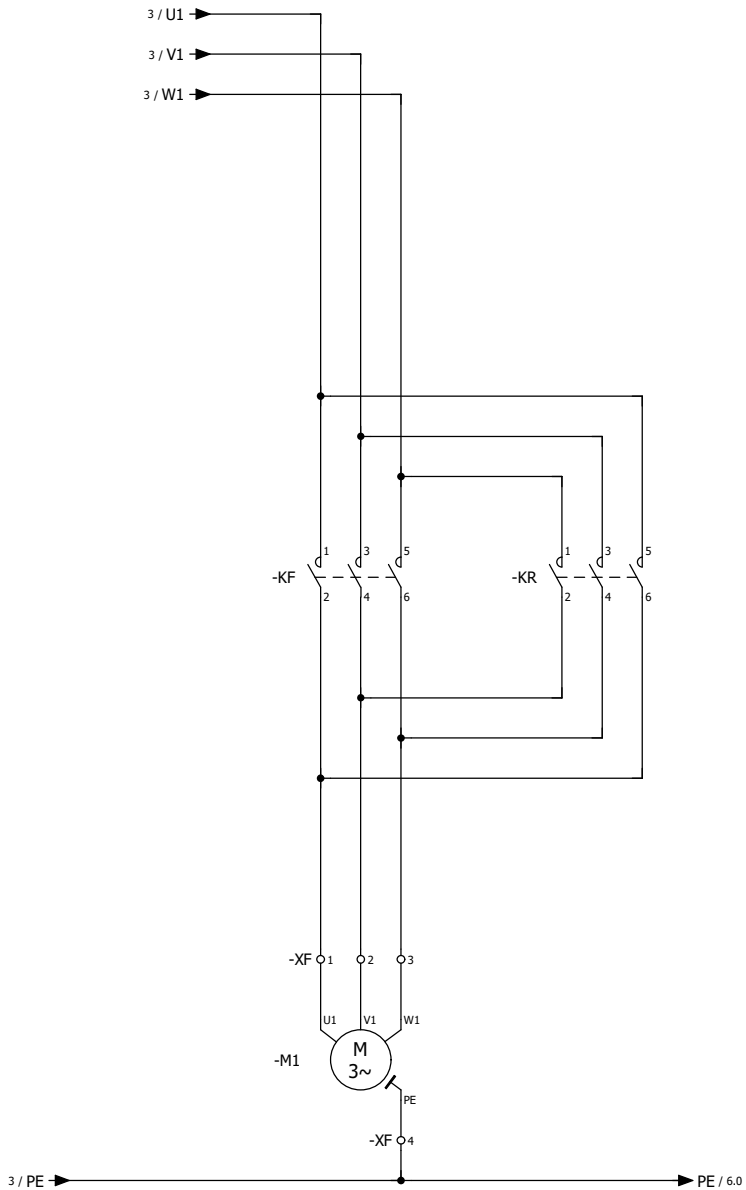


3 5


			Date	10/28/2026	EPLAN		geranito	motor_power	= CA1
			Ed.	PC					+ EAA
			Appr.		graduation project				IEC_bas001 Page 4
Modification	Date	Name	Original		Replacement of	Replaced by			Page 4 / 11

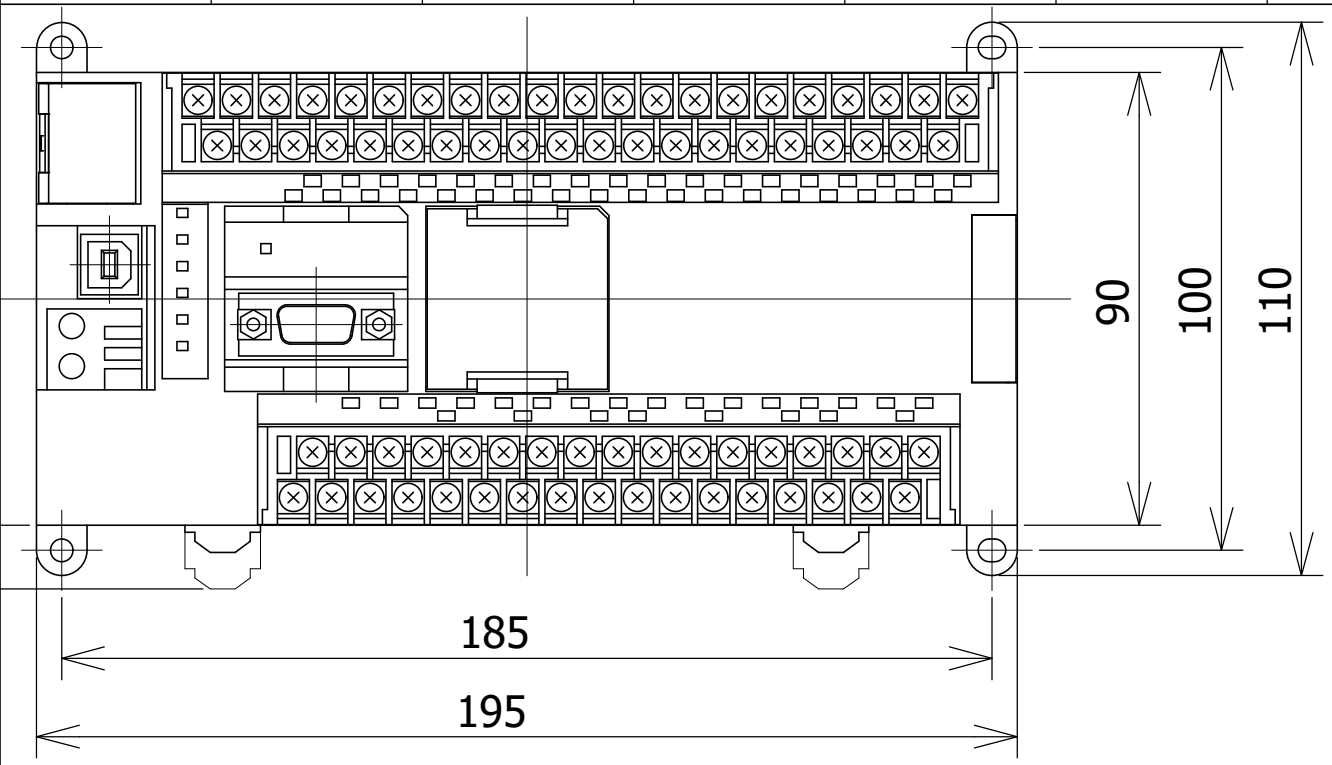

OUTPUTS

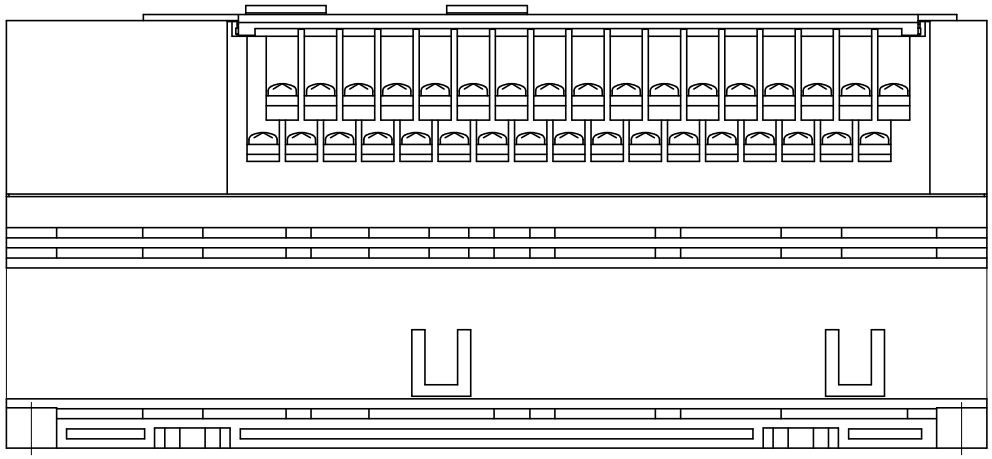


INPUTS

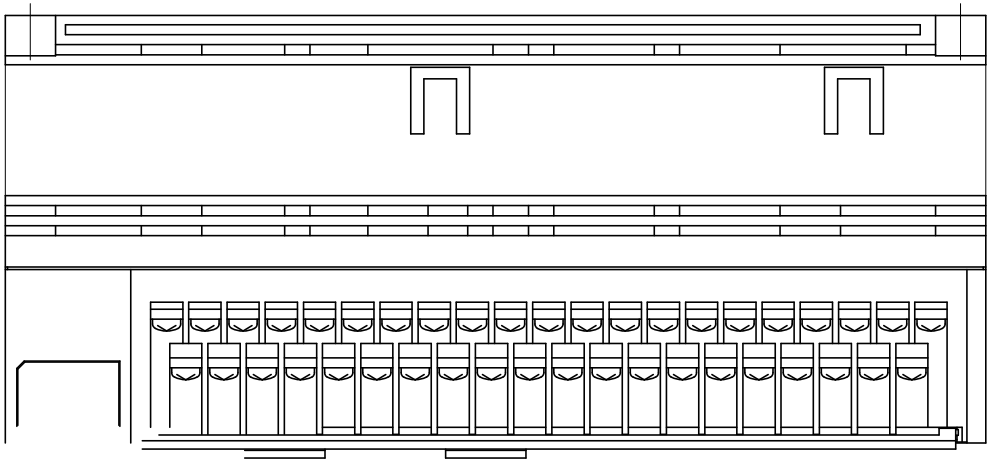


			Date	10/28/2026	EPLAN	geranito	PLC		= CA1
			Ed.	PC					+ EAA
			Appr.		graduation project			IEC_bas001	Page 5
Modification	Date	Name	Original		Replacement of	Replaced by			Page 5 / 11

3 / N
3 / L1
4.5 / PE
/ +24V
/ -24V


N / 7.0
L1 / 7.0
PE / 11.0
+24V / 7.0
-24V / 7.0

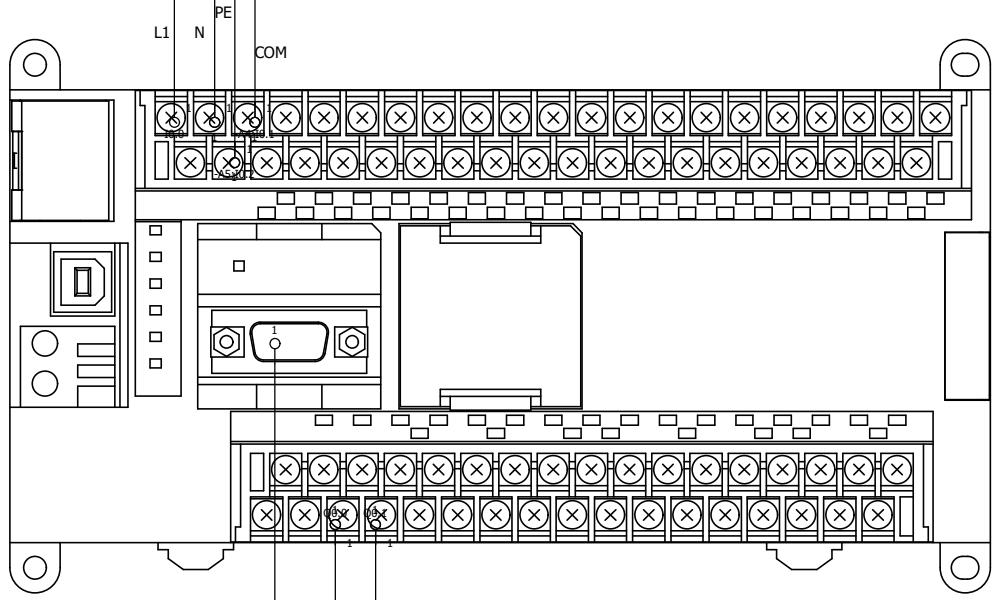
L1
N
PE
COM
1
2
3
4
5
6
7
8
9
10
11
12
13
14
15
16
17
18
19
20
1
2
3
4
5
6
7
8
9
10
11
12
13
14
15
16
17
18
19
20
1
1
1

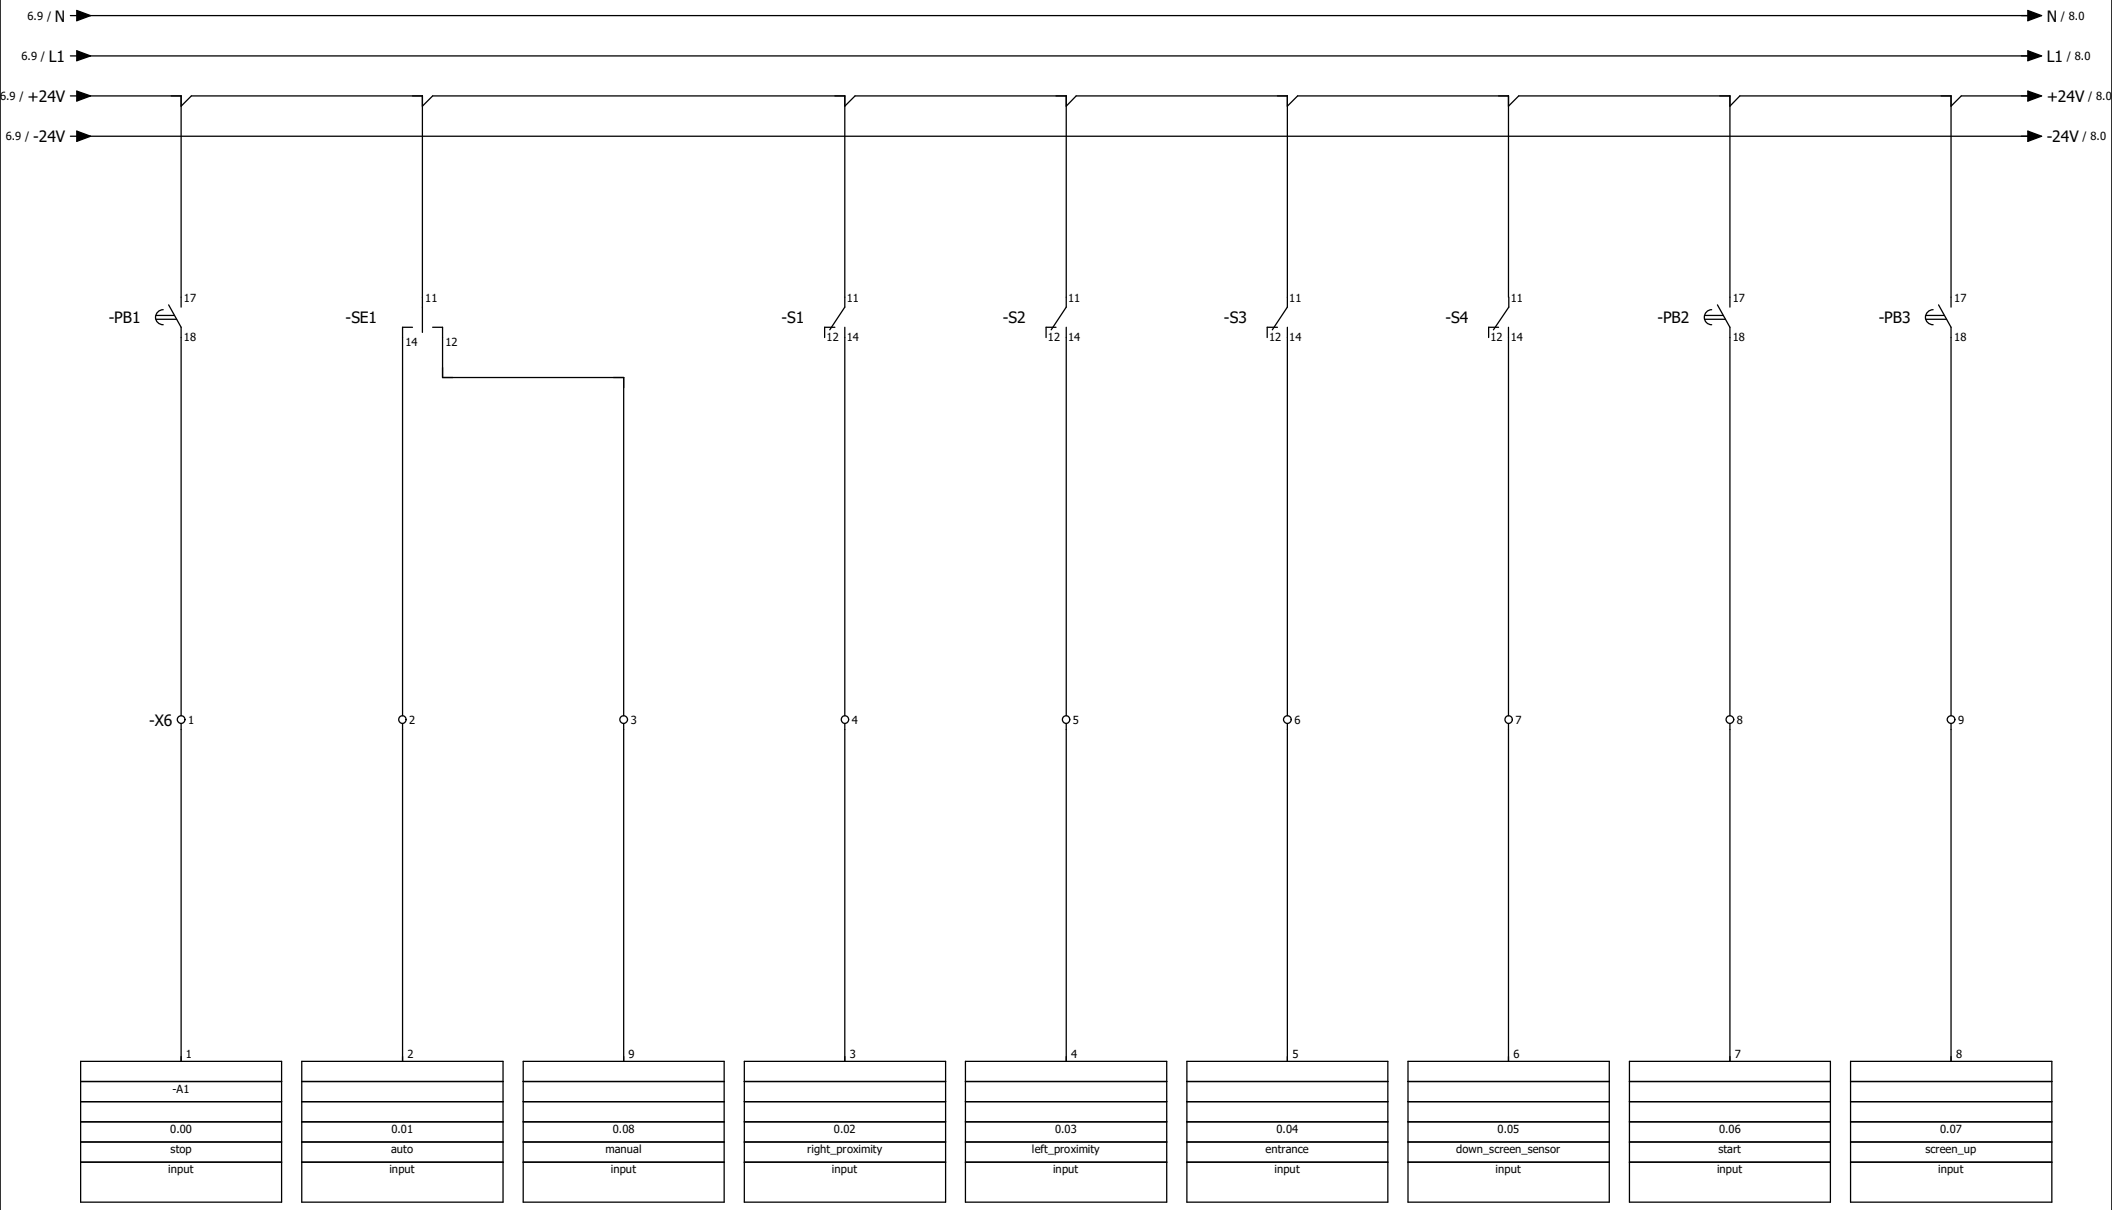


6 8


			Date	10/28/2026	EPLAN	geranito	INPUTS_1	= CA1
			Ed.	PC				+ EAA
			Appr.		graduation project			IEC_bas001 Page 7
Modification	Date	Name	Original		Replacement of	Replaced by		Page 7 / 11

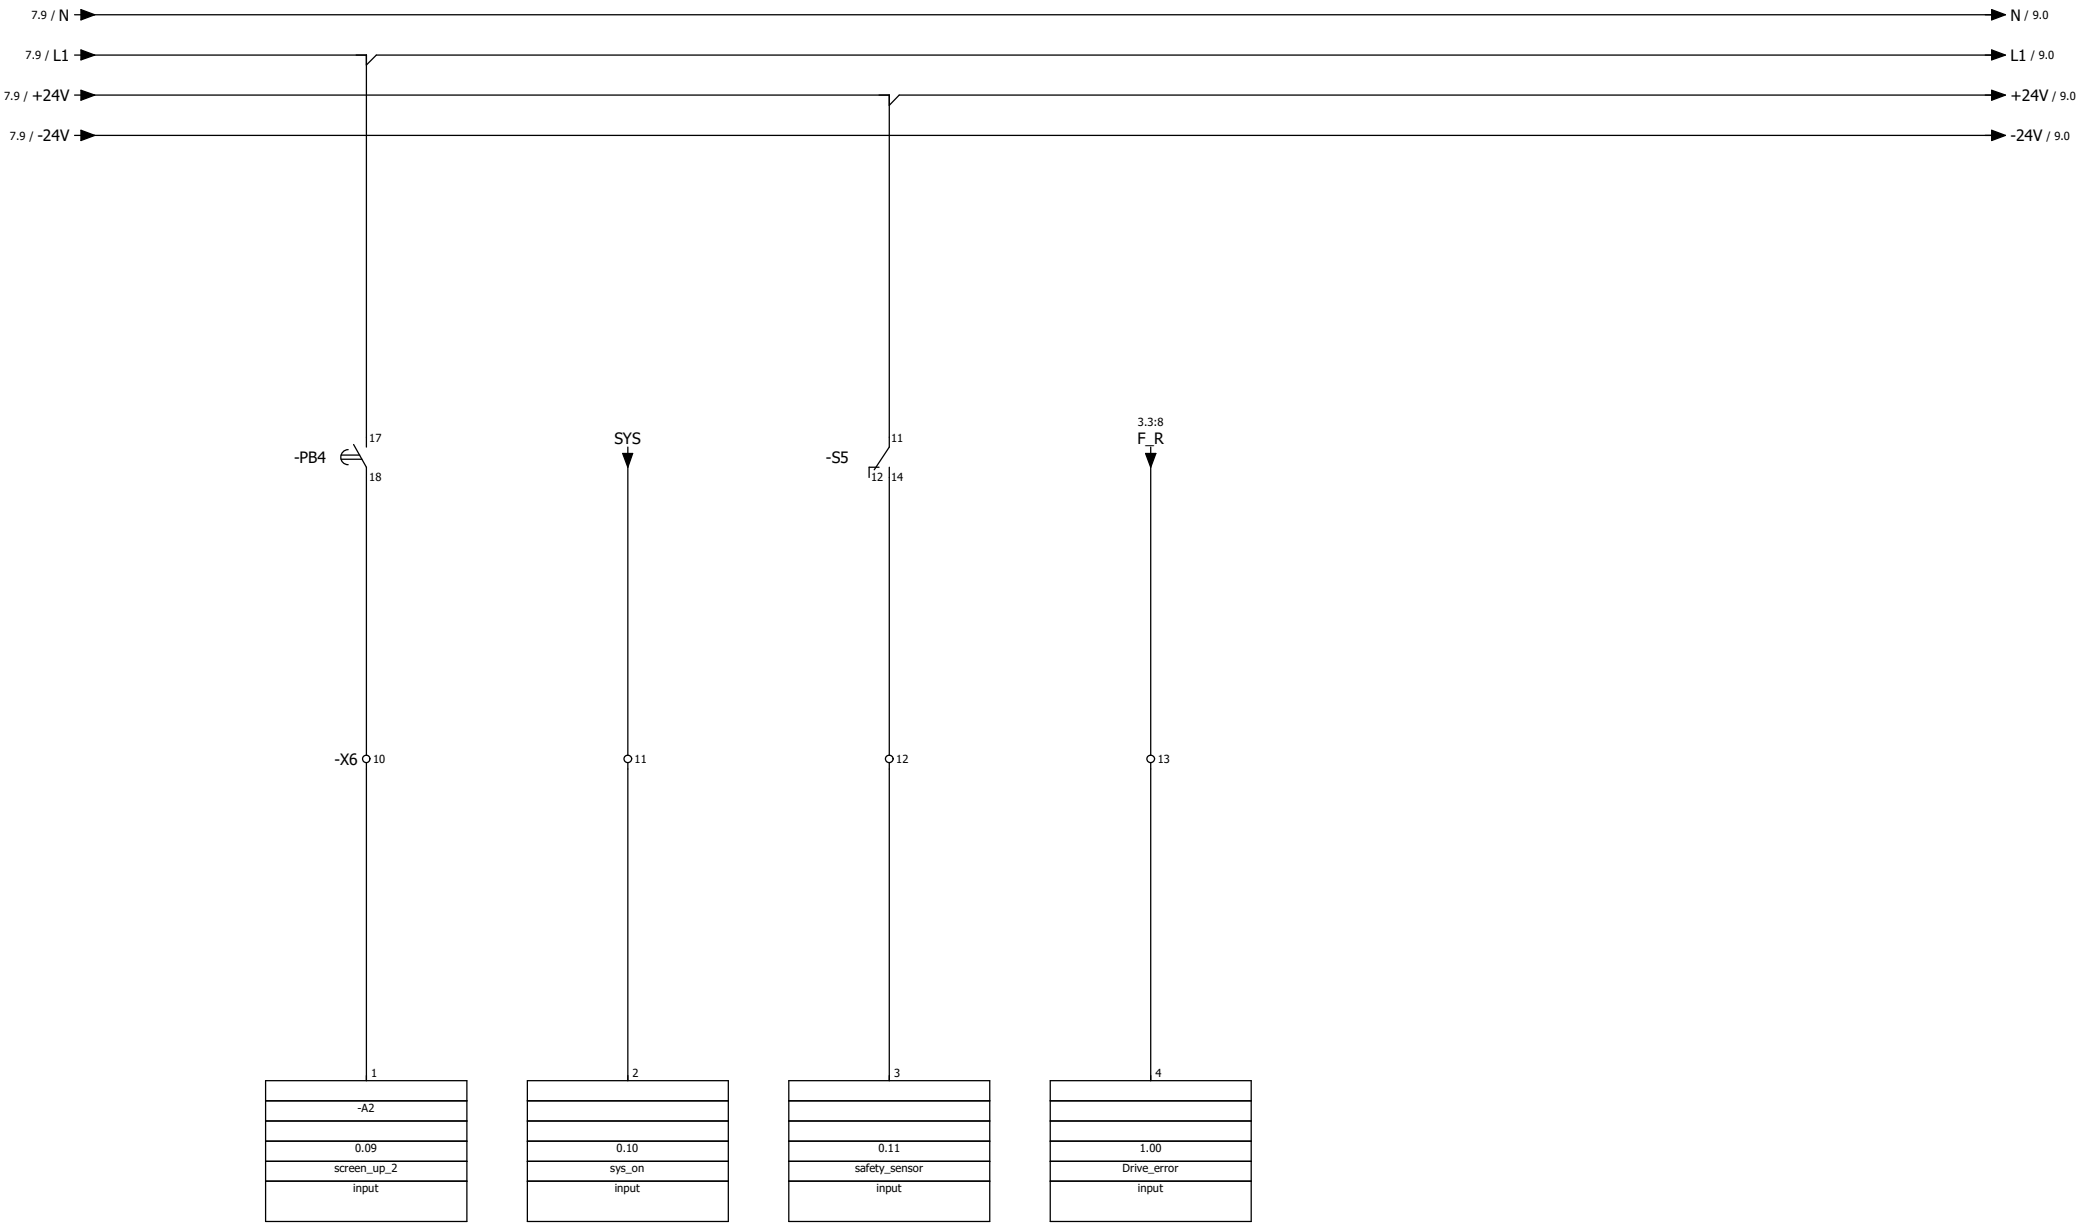

			Date	10/28/2026	EPLAN	geranito	INPUTS_2	= CA1
			Ed.	PC				+ EAA
			Appr.		graduation project			IEC_bas001 Page 8
Modification	Date	Name	Original		Replacement of	Replaced by		Page 8 / 11

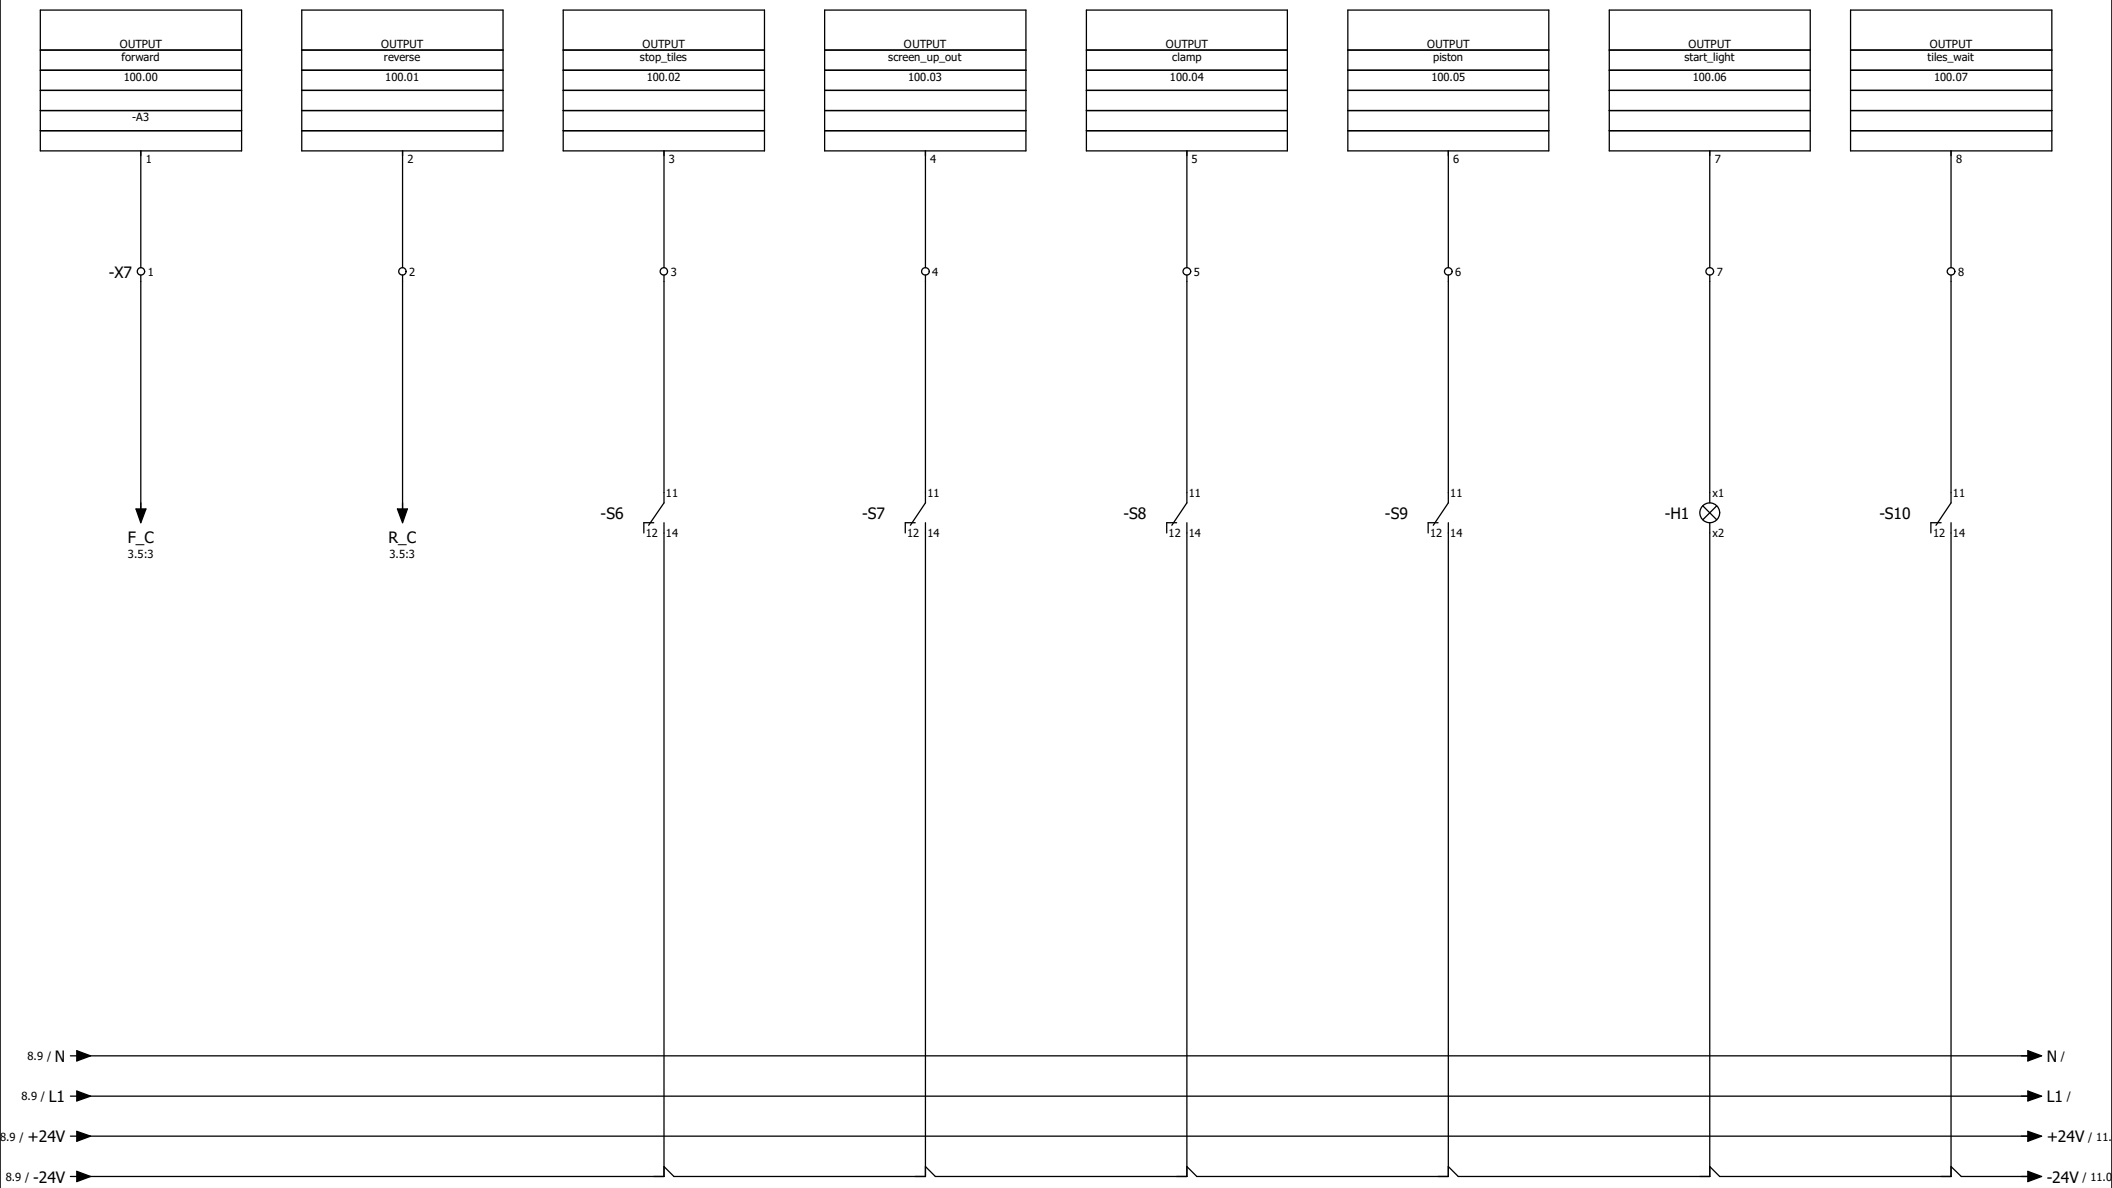

			Date	10/28/2026	EPLAN	geranito	OUTPUTS	= CA1
			Ed.	PC				+ EAA
			Appr.		graduation project			IEC_bas001 Page 9
Modification	Date	Name	Original		Replacement of / Replaced by			Page 9 / 11

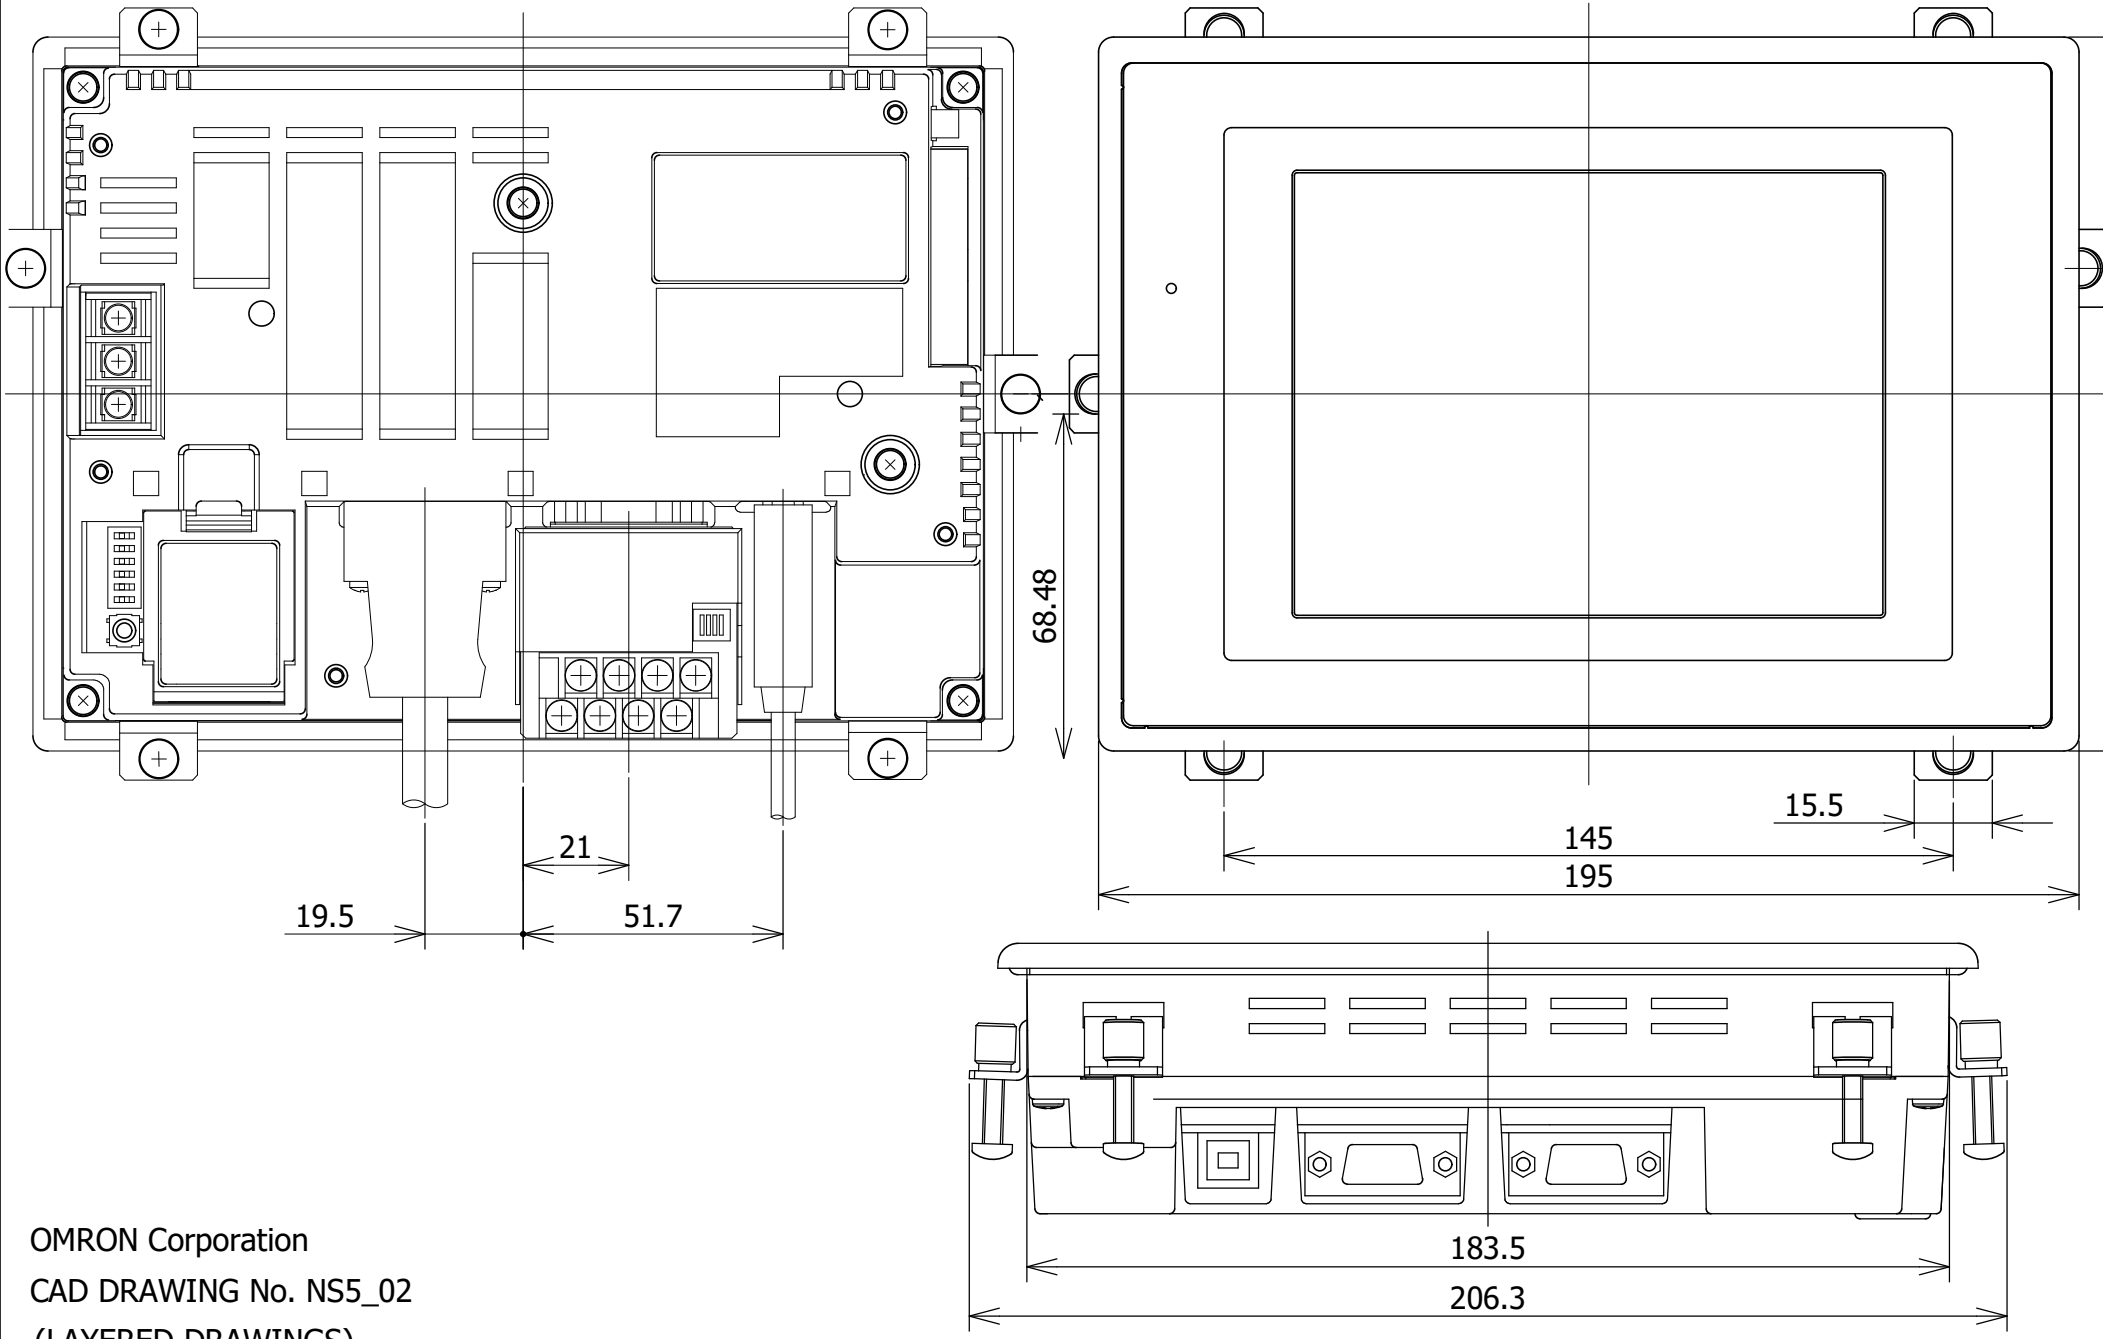


OMRON Corporation

CAD DRAWING No. NS5_02

(LAYERED DRAWINGS)

			Date	10/28/2026	EPLAN	geranito	HMI		= CA1	
			Ed.	PC					+ EAA	
			Appr.		graduation project			IEC_bas001	Page	10
Modification	Date	Name	Original		Replacement of	Replaced by			Page	10 / 11

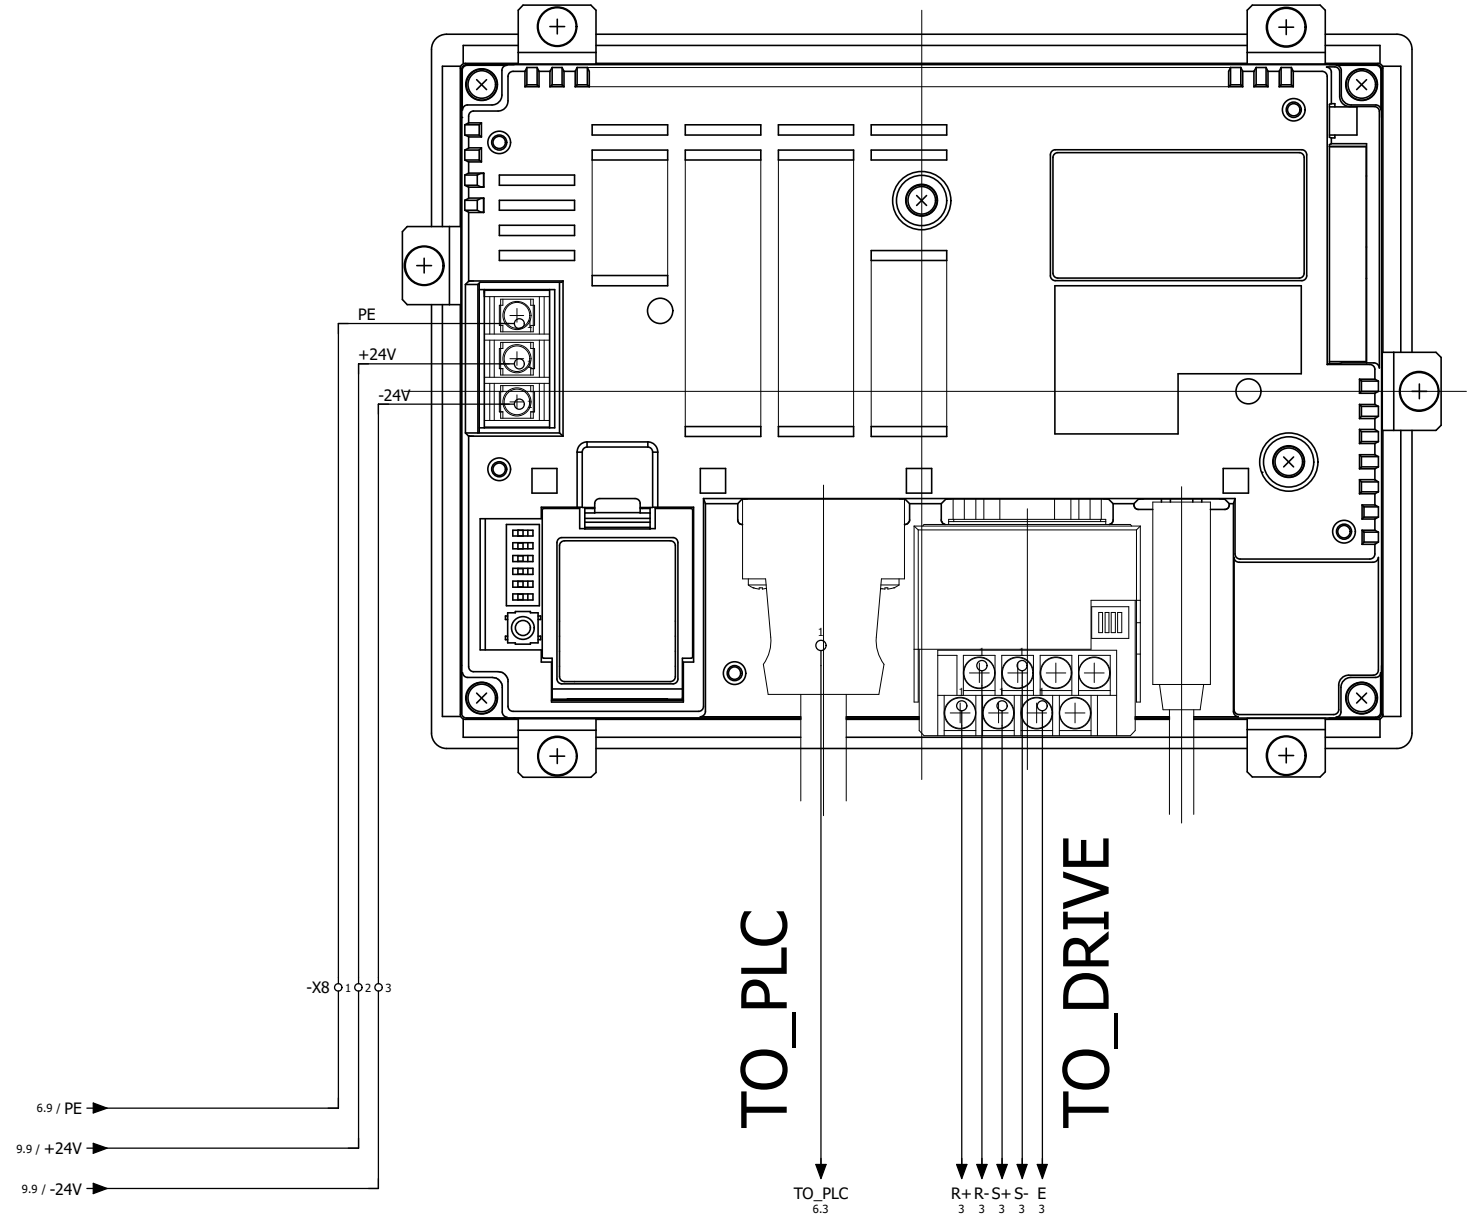

10

			Date	10/28/2026	EPLAN		geranito	HMI_POWER	= CA1
			Ed.	PC					+ EAA
			Appr.		graduation project			IEC_bas001	Page 11
Modification	Date	Name	Original		Replacement of	Replaced by			Page 11 / 11